План размещения осветительных приборов, привязка выпусков освещения 1 этаж

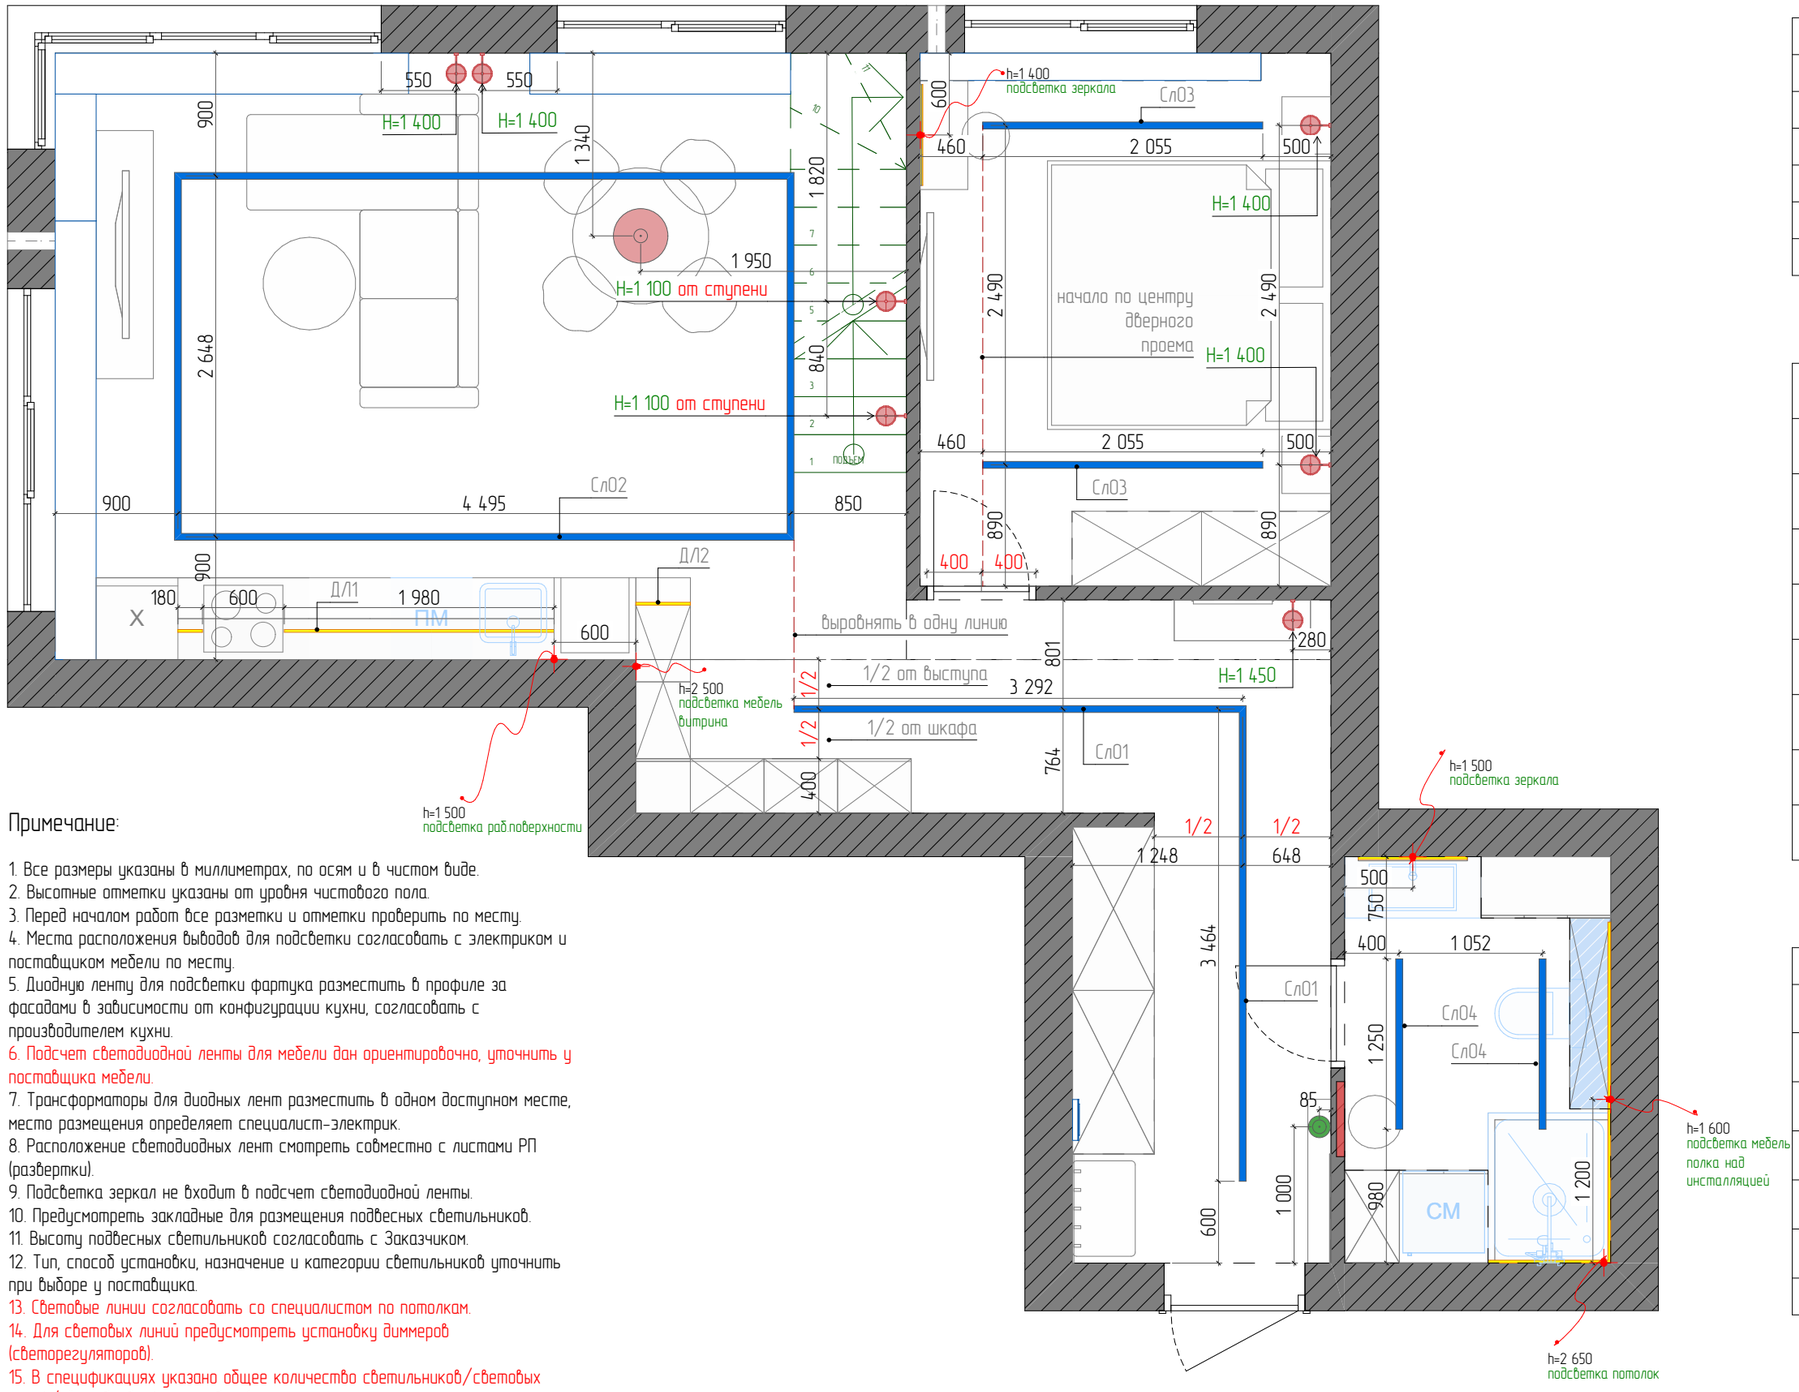

Условное обозначение светильников. (1 этаж + антресоль)			
ID	Изображение	Тип светильника	Кол-во
С-1		люстра	1
С-2		бра	7
С-3		подвесной светильник	1
Эв		электровывод для подсветки	8
			17

LED лента (1 этаж + антресоль)			
ID	Условное обозначение	Наименование	Длина, мм
ДЛ1		кухня рабочая поверхность	2 160
ДЛ2		кухня мебель витрина	2 400
ДЛ3		санузел потолок	2 000
ДЛ4		санузел мебель инсталляция	1 400
ДЛ5		кабинет мебель витрина	1 500
ДЛ6		верт.подсветка кабинет	6 240
			15 700 мм

Спецификация трека/шинопровода (1 этаж + антресоль)			
ID	Условное обозначение	Наименование	Длина, мм
СлО1		Световая линия прихожая	6 782
СлО2		Световая линия кухня-гостиная	14 486
СлО3		Световая линия спальня	4 110
СлО4		Световая линия санузел	2 500
СлО5		Световая линия кабинет	3 928
			31 806 мм

Примечание:

1. Все размеры указаны в миллиметрах, по осям и в чистом виде.
2. Высотные отметки указаны от уровня чистового пола.
3. Перед началом работ все разметки и отметки проверить по месту.
4. Места расположения выводов для подсветки согласовать с электриком и поставщиком мебели по месту.
5. Диодную ленту для подсветки фартука разместить в профиле за фасадами в зависимости от конфигурации кухни, согласовать с производителем кухни.
6. Подсчет светодиодной ленты для мебели дан ориентировочно, уточнить у поставщика мебели.
7. Трансформаторы для диодных лент разместить в одном доступном месте, место размещения определяет специалист-электрик.
8. Расположение светодиодных лент смотреть совместно с листами РП (развертки).
9. Подсветка зеркал не входит в подсчет светодиодной ленты.
10. Предусмотреть закладные для размещения подвесных светильников.
11. Высоту подвесных светильников согласовать с Заказчиком.
12. Тип, способ установки, назначение и категории светильников уточнить при выборе у поставщика.
13. Световые линии согласовать со специалистом по потолкам.
14. Для световых линий предусмотреть установку диммеров (светорегуляторов).
15. В спецификациях указано общее количество светильников/световых линий/светодиодной ленты для 1 этажа и антресоли.

Проект	гп Новоселье, Бульвар Белых ночей, д.3, кв.319	План размещения осветительных приборов, привязка выпусков освещения 1 этаж	Масштаб	Лист	Листов
Дизайнер	Ирина Лобанова		1:45	13	63
телефон	+7-953-902-05-38		Дата	16.03.2026	

План размещения осветительных приборов, привязка выпусков освещения (антресоль)

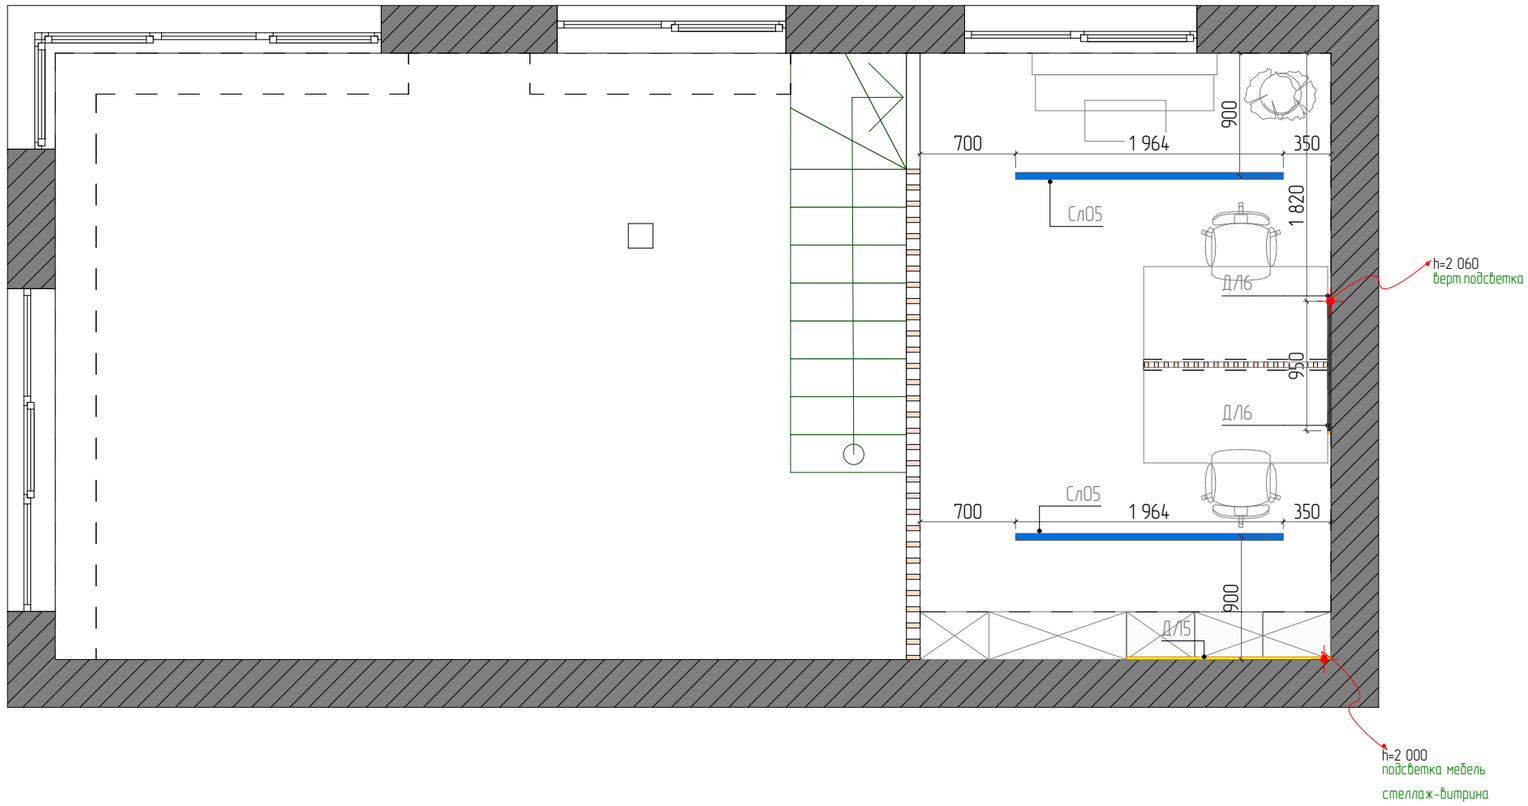

Условное обозначение светильников. (1 этаж + антресоль)			
ID	Изображение	Тип светильника	Кол-во
С-1		люстра	1
С-2		бра	7
С-3		подвесной светильник	1
Эв		электровывод для подсветки	8
			17

LED лента (1 этаж + антресоль)			
ID	Условное обозначение	Наименование	Длина, мм
ДЛ1		кухня рабочая поверхность	2 160
ДЛ2		кухня мебель витрина	2 400
ДЛ3		санузел потолок	2 000
ДЛ4		санузел мебель инсталляция	1 400
ДЛ5		кабинет мебель витрина	1 500
ДЛ6		верт.подсветка кабинет	6 240
			15 700 мм

Спецификация трека/шинопровода (1 этаж + антресоль)			
ID	Условное обозначение	Наименование	Длина, мм
СлО1		Световая линия прихожая	6 782
СлО2		Световая линия кухня-гостиная	14 486
СлО3		Световая линия спальня	4 110
СлО4		Световая линия санузел	2 500
СлО5		Световая линия кабинет	3 928
			31 806 мм

Примечание:

1. Все размеры указаны в миллиметрах, по осям и в чистом виде.
2. Высотные отметки указаны от уровня чистового пола.
3. Перед началом работ все разметки и отметки проверить по месту.
4. Места расположения выводов для подсветки согласовать с электриком и поставщиком мебели по месту.
5. Диодную ленту для подсветки фартука разместить в профиле за фасадами в зависимости от конфигурации кухни, согласовать с производителем кухни.
6. Подсчет светодиодной ленты для мебели дан ориентировочно, уточнить у поставщика мебели.
7. Трансформаторы для диодных лент разместить в одном доступном месте, место размещения определяет специалист-электрик.
8. Расположение светодиодных лент смотреть совместно с листами РП (развертки).
9. Подсветка зеркал не входит в подсчет светодиодной ленты.
10. Предусмотреть закладные для размещения подвесных светильников.
11. Высоту подвесных светильников согласовать с Заказчиком.
12. Тип, способ установки, назначение и категории светильников уточнить при выборе у поставщика.
13. Световые линии согласовать со специалистом по потолкам.
14. Для световых линий предусмотреть установку диммеров (светорегуляторов).
15. В спецификациях указано общее количество светильников/световых линий/светодиодной ленты для 1 этажа и антресоли.

Проект	гп Новоселье, Бульвар Белых ночей, д.3, кв.319	План размещения осветительных приборов, привязка выпусков освещения (антресоль)	Масштаб	Лист	Листов
Дизайнер	Ирина Лобанова		1:45	14	63
телефон	+7-953-902-05-38		Дата	16.03.2026	

План выключателей с указанием включения групп светильников 1 этаж

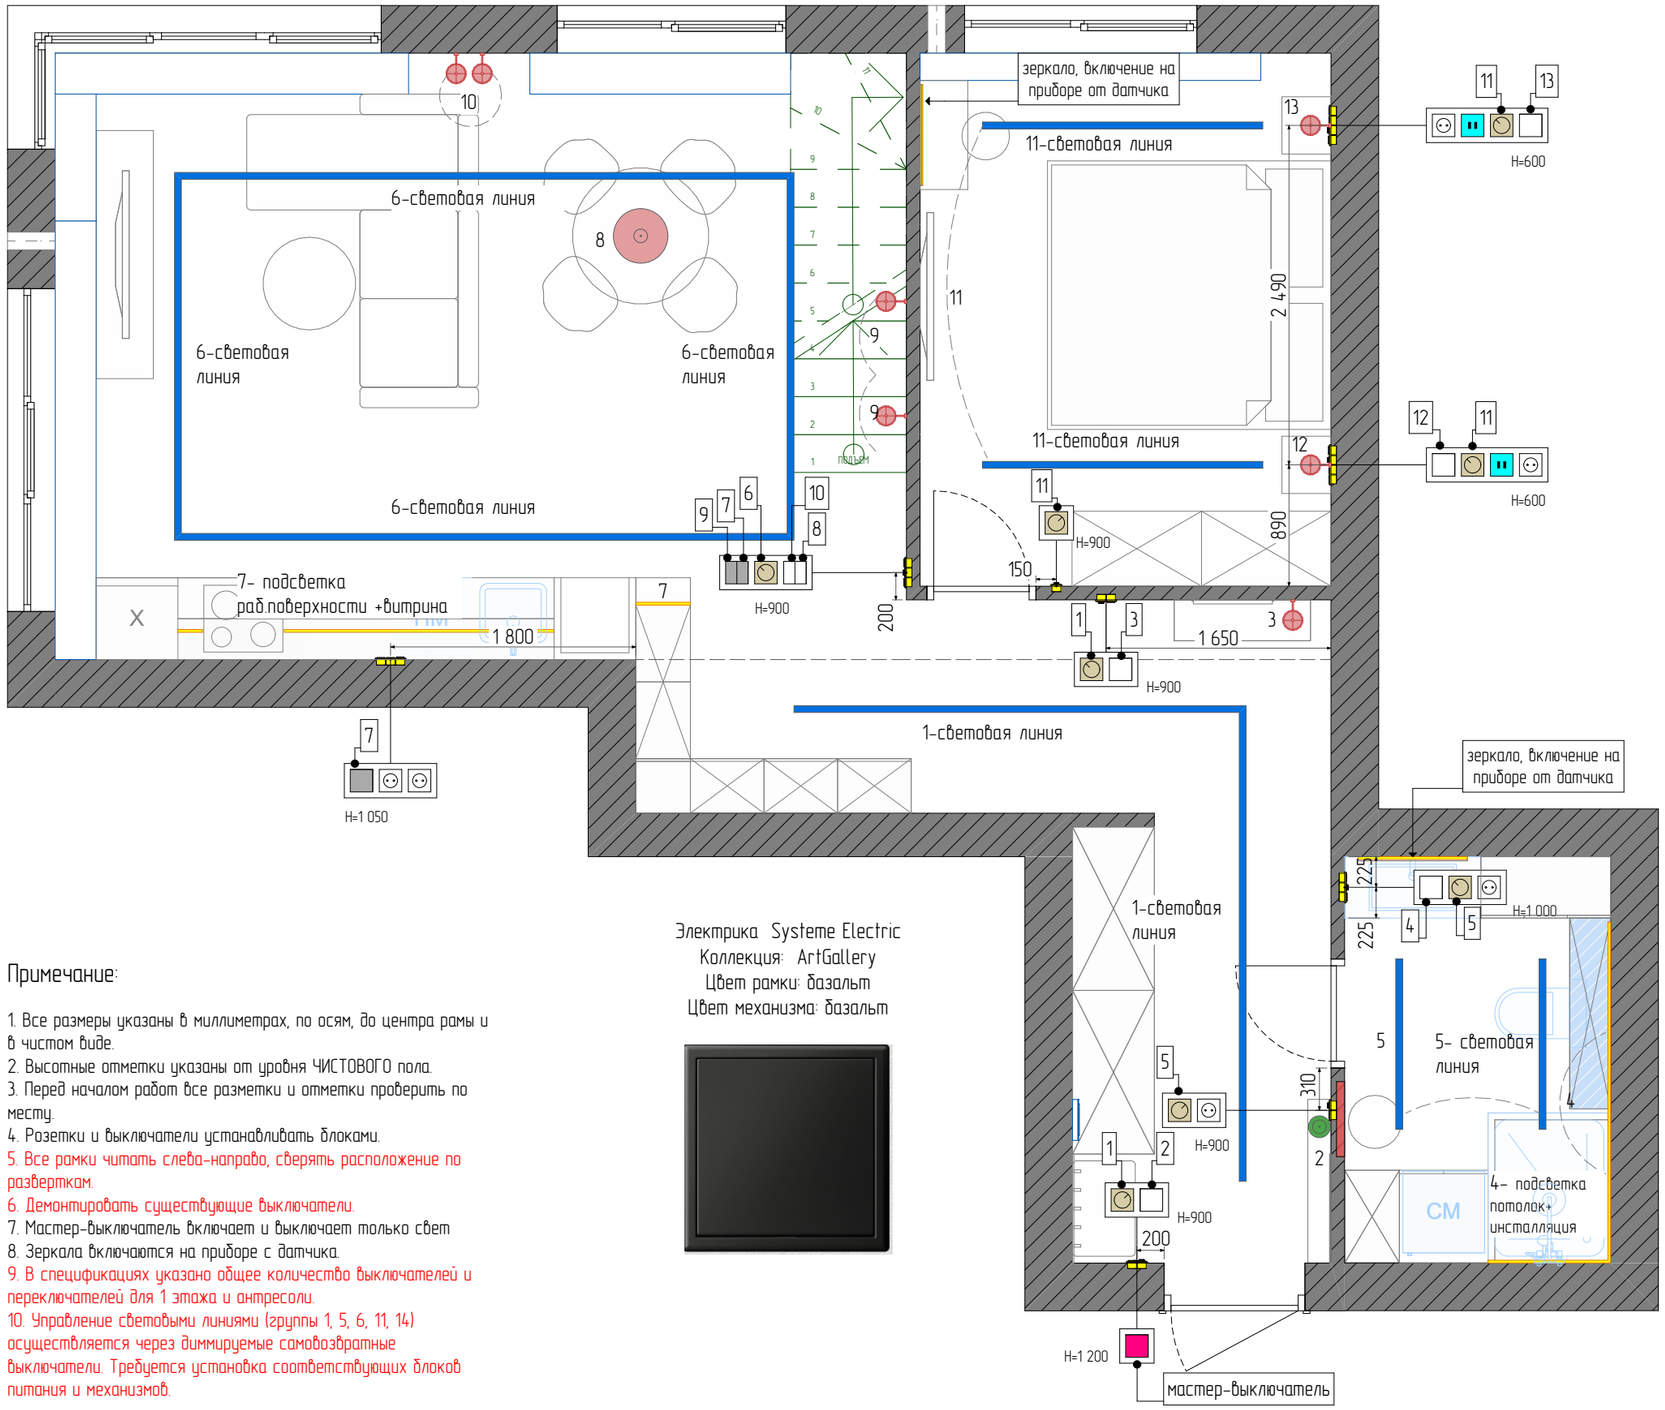

Электрика Systeme Electric
Коллекция: ArtGallery
Цвет рамки: базальт
Цвет механизма: базальт

Примечание:

1. Все размеры указаны в миллиметрах, по осям, до центра рамы и в чистом виде.
2. Высотные отметки указаны от уровня ЧИСТОВОГО пола.
3. Перед началом работ все разметки и отметки проверить по месту.
4. Розетки и выключатели устанавливать блоками.
5. Все рамки читать слева-направо, сверять расположение по развертках.
6. Демонтировать существующие выключатели.
7. Мастер-выключатель включает и выключает только свет
8. Зеркала включаются на приборе с датчика.
9. В спецификациях указано общее количество выключателей и переключателей для 1 этажа и антресоли.
10. Управление световыми линиями (группы 1, 5, 6, 11, 14) осуществляется через диммируемые самовозвратные выключатели. Требуется установка соответствующих блоков питания и механизмов.

Выключатели 1 этаж+ антресоль		
Условное обозначение	Наименование	Кол-во, шт
	Выключатель двухклавишный	1
	Выключатель двухклавишный проходной	2
	Выключатель одноклавишный	5
	Выключатель одноклавишный проходной	3
	Мастер-выключатель	1
	Самовозвратный выключатель	9

Проект	гп Новоселье, Бульвар Белых ночей, д.3, кв.319	План выключателей с указанием включения групп светильников 1 этаж	Масштаб	Лист	Листов
Дизайнер	Ирина Лобанова		1:45	15	63
телефон	+7-953-902-05-38		Дата	16.03.2026	

План выключателей с указанием включения групп светильников антресоль

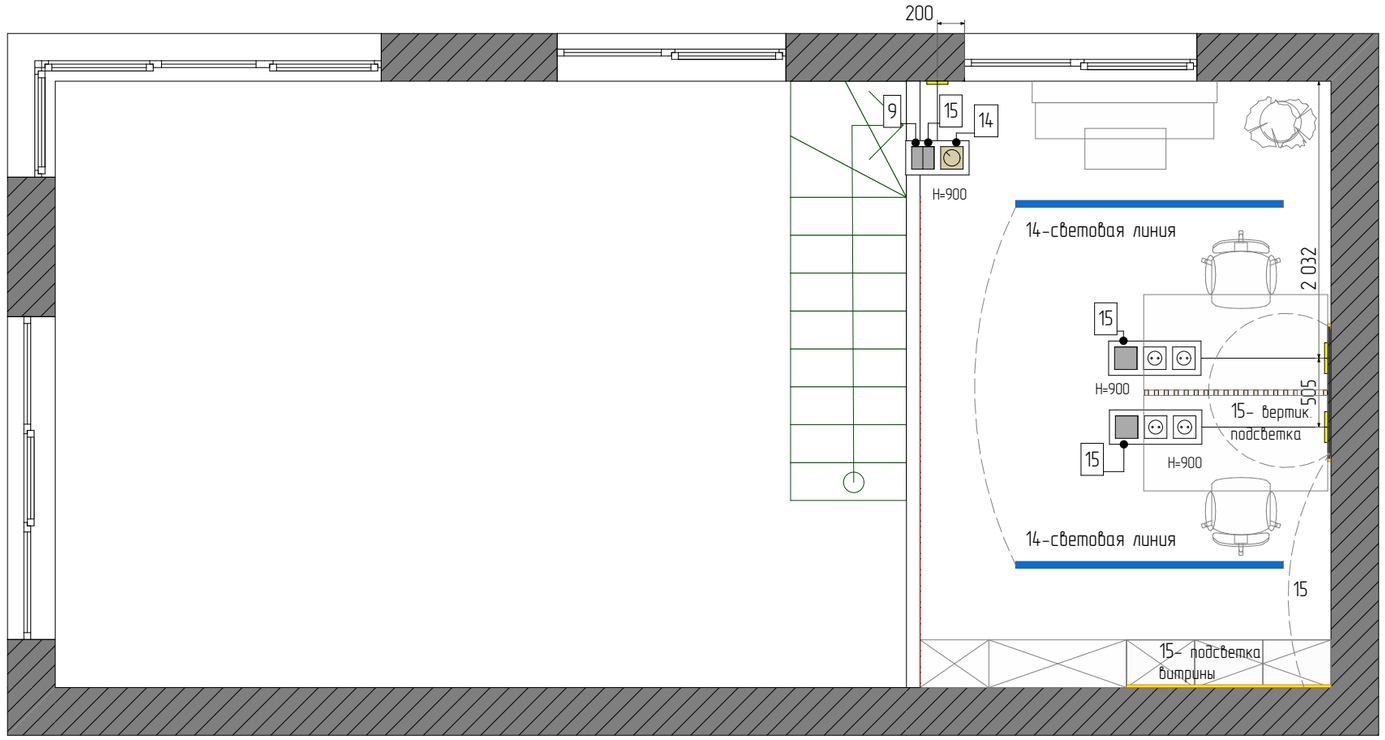

Электрика Systeme Electric
Коллекция: ArtGallery
Цвет рамки: базальт
Цвет механизма: базальт

Примечание:

1. Все размеры указаны в миллиметрах, по осям, до центра рамы и в чистом виде.
2. Высотные отметки указаны от уровня ЧИСТОВОГО пола.
3. Перед началом работ все разметки и отметки проверить по месту.
4. Розетки и выключатели устанавливать блоками.
5. Все рамки читать слева-направо, сверять расположение по развертках.
6. Демонтировать существующие выключатели.
7. Мастер-выключатель включает и выключает только свет
8. Зеркала включаются на приборе с датчика.
9. В спецификациях указано общее количество выключателей и переключателей для 1 этажа и антресоли.
10. Управление световыми линиями (группы 1, 5, 6, 11, 14) осуществляется через диммируемые самовозвратные выключатели. Требуется установка соответствующих блоков питания и механизмов.

Выключатели 1 этаж+ антресоль		
Условное обозначение	Наименование	Кол-во, шт
	Выключатель двухклавишный	1
	Выключатель двухклавишный проходной	2
	Выключатель одноклавишный	5
	Выключатель одноклавишный проходной	3
	Мастер-выключатель	1
	Самовозвратный выключатель	9

Проект	гп Новоселье, Бульвар Белых ночей, д.3, кв.319	План выключателей с указанием включения групп светильников антресоль	Масштаб	Лист	Листов
Дизайнер	Ирина Лобанова		1:45	16	63
телефон	+7-953-902-05-38		Дата	16.03.2026	

План размещения электрических розеток с привязкой размеров 1 этаж

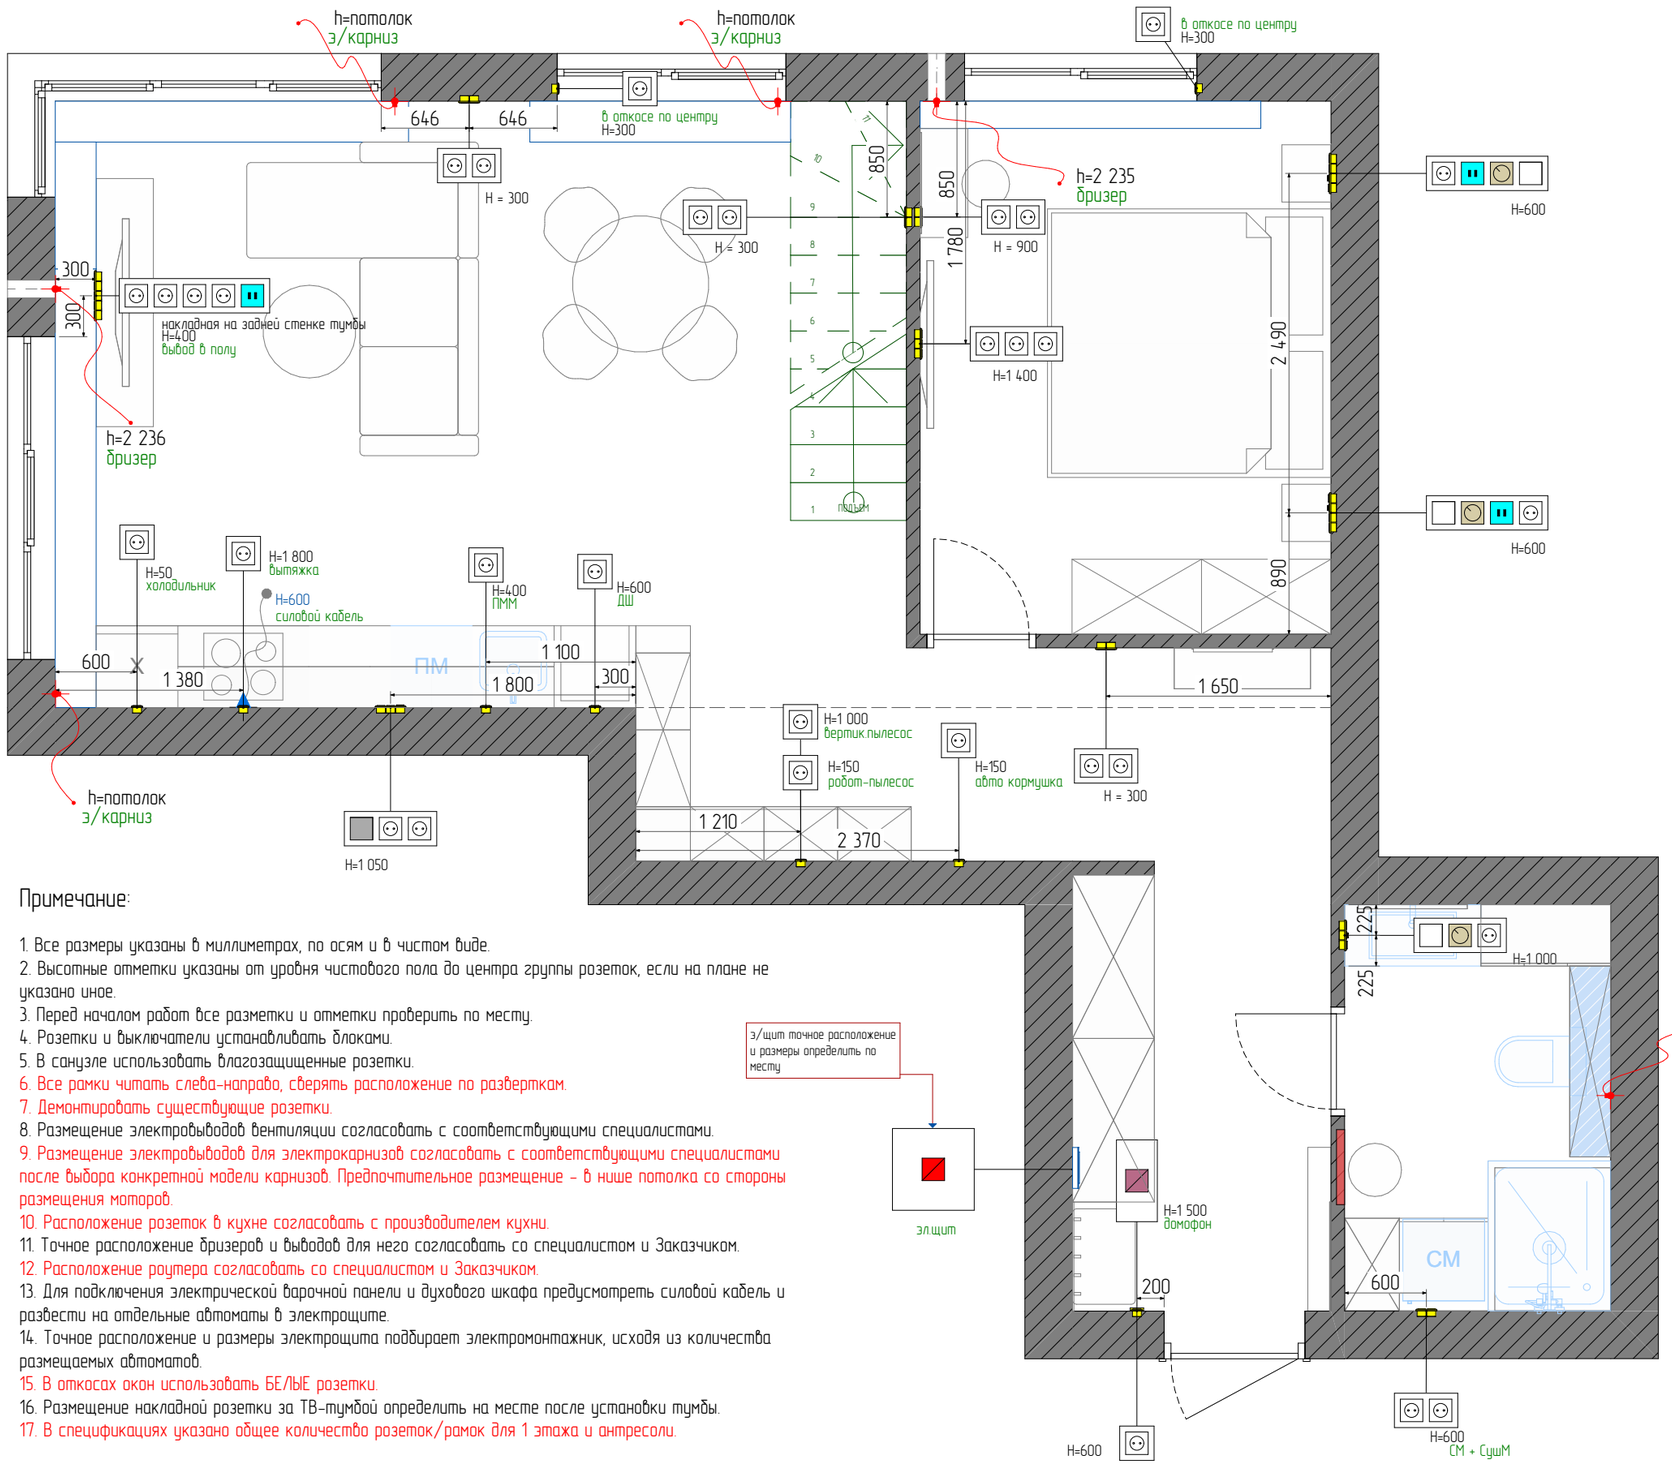

Условное обозначение	Наименование	Кол-во, шт
	Вывод для домофона	1
	Интернет-розетка RJ45	1
	Розетка 220V + USB	3
	Розетка бытовая 220 V	46
	Силовой кабель	1
	Эл.щит/слаботочный щит	1
	Электровывод	6

Рамки (общее количество)		
Тип рамки (блока)	Рамка ориентация	Кол-во
Рамка x1	Горизонтальная	15
Рамка x2	Горизонтальная	11
Рамка x3	Горизонтальная	7
Рамка x4	Горизонтальная	2
Рамка x5	Горизонтальная	1
		36

Примечание:

1. Все размеры указаны в миллиметрах, по осям и в чистом виде.
2. Высотные отметки указаны от уровня чистового пола до центра группы розеток, если на плане не указано иное.
3. Перед началом работ все разметки и отметки проверить по месту.
4. Розетки и выключатели устанавливать блоками.
5. В санузле использовать влагозащищенные розетки.
6. Все рамки читать слева-направо, сверять расположение по разверткам.
7. Демонтировать существующие розетки.
8. Размещение электровыводов вентиляции согласовать с соответствующими специалистами.
9. Размещение электровыводов для электрокарнизов согласовать с соответствующими специалистами после выбора конкретной модели карнизов. Предпочтительное размещение - в нише потолка со стороны размещения моторов.
10. Расположение розеток в кухне согласовать с производителем кухни.
11. Точное расположение бризеров и выводов для него согласовать со специалистом и Заказчиком.
12. Расположение роутера согласовать со специалистом и Заказчиком.
13. Для подключения электрической варочной панели и духового шкафа предусмотреть силовой кабель и развести на отдельные автоматы в электрощите.
14. Точное расположение и размеры электрощита подбирает электромонтажник, исходя из количества размещаемых автоматов.
15. В откосах окон использовать БЕЛЫЕ розетки.
16. Размещение накладной розетки за ТВ-тумбой определить на месте после установки тумбы.
17. В спецификациях указано общее количество розеток/рамок для 1 этажа и антресоли.

Электрика Systeme Electric
Коллекция: ArtGallery
Цвет рамки: базальт
Цвет механизма: базальт

Электрика Systeme Electric
Коллекция: ArtGallery
Цвет рамки: белый
Цвет механизма: белый
(в откосах)

Проект	гп Новоселье, Бульвар Белых ночей, д.3, кв.319	План размещения электрических розеток с привязкой размеров 1 этаж	Масштаб	Лист	Листов
Дизайнер	Ирина Лобанова		1:45	17	63
телефон	+7-953-902-05-38		Дата	16.03.2026	

План размещения электрических розеток с привязкой размеров, антресоль

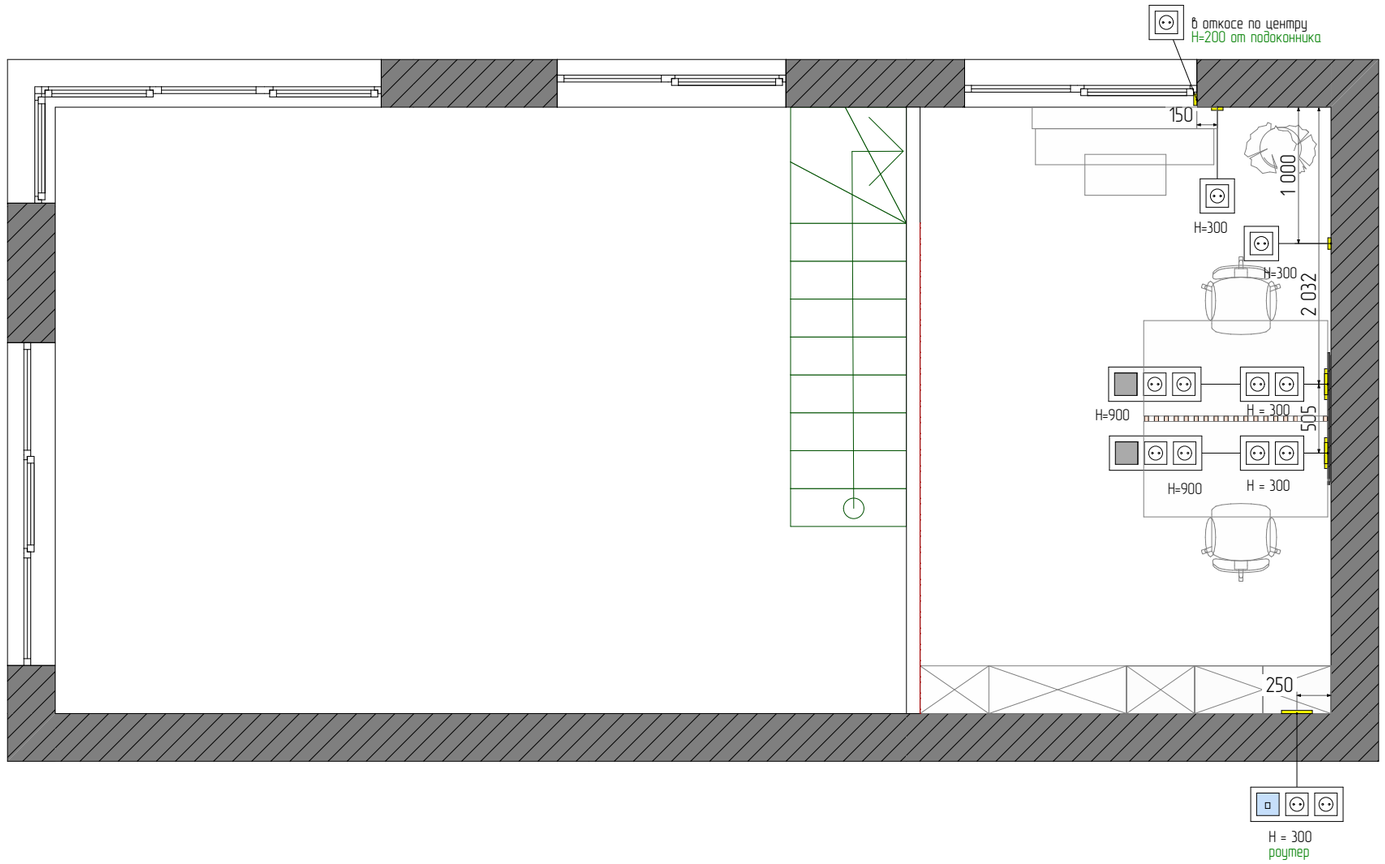

Условное обозначение	Наименование	Кол-во, шт
	Вывод для домофона	1
	Интернет-розетка RJ45	1
	Розетка 220V + USB	3
	Розетка бытовая 220 V	46
	Силовой кабель	1
	Эл.щит/слаботочный щит	1
	Электровывод	6

Рамки (общее количество)		
Тип рамки (блока)	Рамка ориентация	Кол-во
Рамка х1	Горизонтальная	15
Рамка х2	Горизонтальная	11
Рамка х3	Горизонтальная	7
Рамка х4	Горизонтальная	2
Рамка х5	Горизонтальная	1
		36

Примечание:

1. Все размеры указаны в миллиметрах, по осям и в чистом виде.
2. Высотные отметки указаны от уровня чистового пола до центра группы розеток, если на плане не указано иное.
3. Перед началом работ все разметки и отметки проверить по месту.
4. Розетки и выключатели устанавливать блоками.
5. В санузле использовать влагозащищенные розетки.
6. Все рамки читать слева-направо, сверять расположение по разверткам.
7. Демонтировать существующие розетки.
8. Размещение электровыводов вентиляции согласовать с соответствующими специалистами.
9. Размещение электровыводов для электрокарнизов согласовать с соответствующими специалистами после выбора конкретной модели карнизов. Предпочтительное размещение - в нише потолка со стороны размещения моторов.
10. Расположение розеток в кухне согласовать с производителем кухни.
11. Точное расположение бризеров и выводов для него согласовать со специалистом и Заказчиком.
12. Расположение роутера согласовать со специалистом и Заказчиком.
13. Для подключения электрической варочной панели и духового шкафа предусмотреть силовой кабель и развести на отдельные автоматы в электрощите.
14. Точное расположение и размеры электрощита подбирает электромонтажник, исходя из количества размещаемых автоматов.
15. В откосах окон использовать БЕЛЫЕ розетки.
16. Размещение накладной розетки за ТВ-тумбой определить на месте после установки тумбы.
17. В спецификациях указано общее количество розеток/рамок для 1 этажа и антресоли.

Электрика Systeme Electric
Коллекция: ArtGallery
Цвет рамки: базальт
Цвет механизма: базальт

Электрика Systeme Electric
Коллекция: ArtGallery
Цвет рамки: белый
Цвет механизма: белый
(в откосах)

Проект	гп Новоселье, Бульвар Белых ночей, д.3, кв.319	План размещения электрических розеток с привязкой размеров, антресоль	Масштаб	Лист	Листов
Дизайнер	Ирина Лобанова		1:45	18	63
телефон	+7-953-902-05-38		Дата	16.03.2026	

План размещения электрических розеток и выключателей 1 этаж

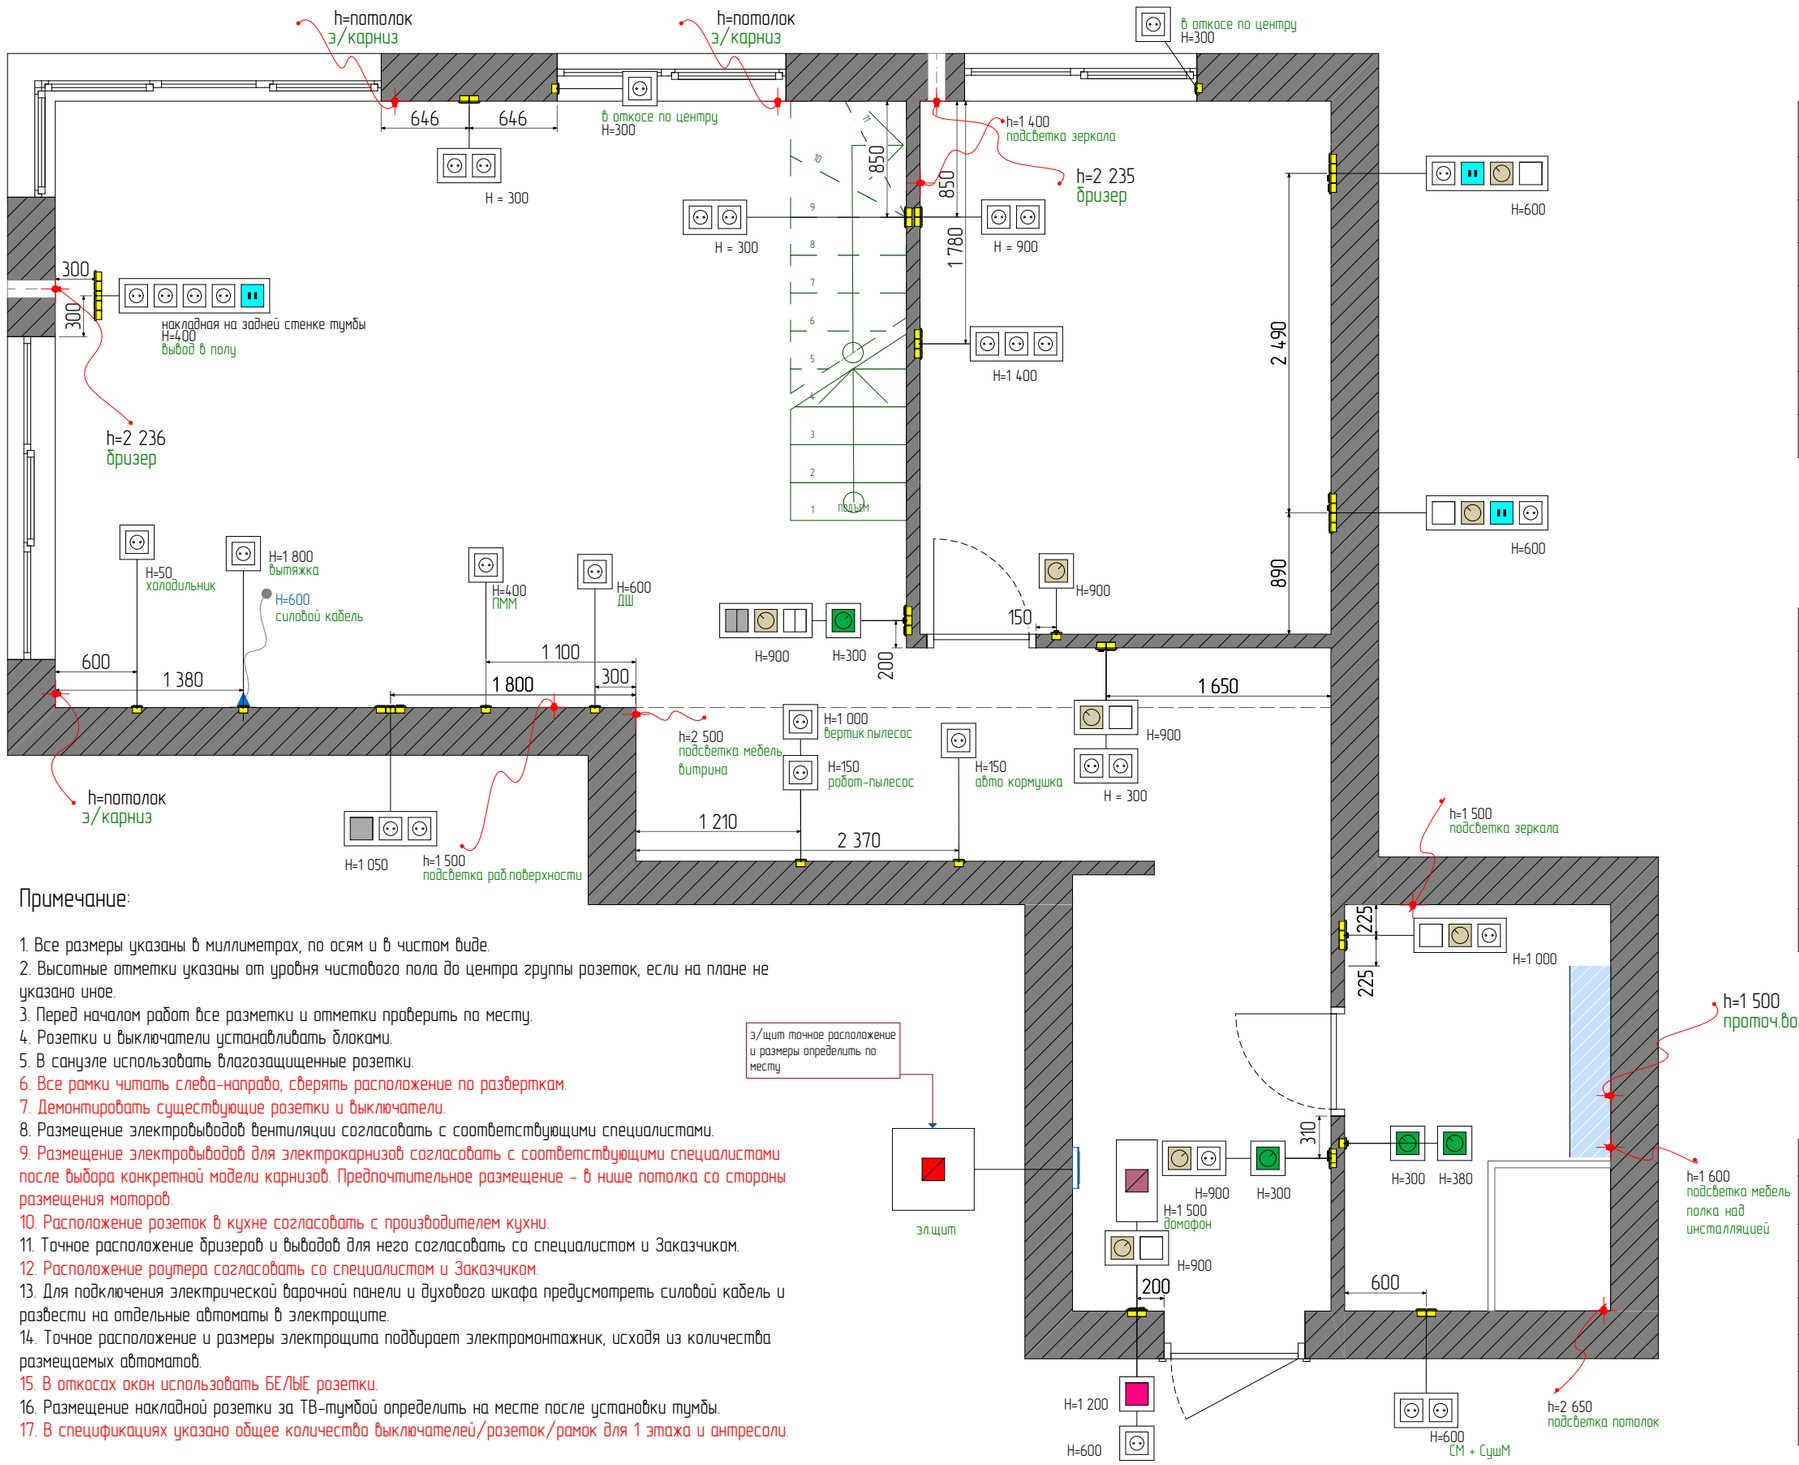

Условное обозначение	Наименование	Кол-во, шт
	Вывод для домофона	1
	Интернет-розетка RJ45	1
	Розетка 220V + USB	3
	Розетка бытовая 220 V	46
	Силовой кабель	1
	Эл.щит/слаботочный щит	1
	Электровывод	15

Выключатели 1 этаж+ антресоль		
Условное обозначение	Наименование	Кол-во, шт
	Выключатель двухклавишный	1
	Выключатель двухклавишный проходной	2
	Выключатель одноклавишный	5
	Выключатель одноклавишный проходной	3
	Мастер-выключатель	1
	Самовозвратный выключатель	9

Примечание:

1. Все размеры указаны в миллиметрах, по осям и в чистом виде.
2. Высотные отметки указаны от уровня чистового пола до центра группы розеток, если на плане не указано иное.
3. Перед началом работ все разметки и отметки проверить по месту.
4. Розетки и выключатели устанавливать блоками.
5. В санузле использовать влагозащищенные розетки.
6. Все рамки читать слева-направо, сверять расположение по разверткам.
7. Демонтировать существующие розетки и выключатели.
8. Размещение электровыводов вентиляции согласовать с соответствующими специалистами.
9. Размещение электровыводов для электрокарнизов согласовать с соответствующими специалистами после выбора конкретной модели карнизов. Предпочтительное размещение - в нише потолка со стороны размещения моторов.
10. Расположение розеток в кухне согласовать с производителем кухни.
11. Точное расположение бризеров и выводов для него согласовать со специалистом и Заказчиком.
12. Расположение роутера согласовать со специалистом и Заказчиком.
13. Для подключения электрической варочной панели и духового шкафа предусмотреть силовой кабель и развести на отдельные автоматы в электрощите.
14. Точное расположение и размеры электрощита подбирает электромонтажник, исходя из количества размещаемых автоматов.
15. В откосах окон использовать БЕЛЫЕ розетки.
16. Размещение накладной розетки за ТВ-тумбой определить на месте после установки тумбы.
17. В спецификациях указано общее количество выключателей/розеток/рамок для 1 этажа и антресоли.

Рамки (общее количество)		
Тип рамки (блока)	Рамка ориентация	Кол-во
Рамка х1	Горизонтальная	15
Рамка х2	Горизонтальная	11
Рамка х3	Горизонтальная	7
Рамка х4	Горизонтальная	2
Рамка х5	Горизонтальная	1
		36

Проект	гп Новоселье, Бульвар Белых ночей, д.3, кв.319	План размещения электрических розеток и выключателей 1 этаж	Масштаб	Лист	Листов
Дизайнер	Ирина Лобанова		1:45	19	63
телефон	+7-953-902-05-38		Дата	16.03.2026	

План размещения электрических розеток и выключателей антресоль

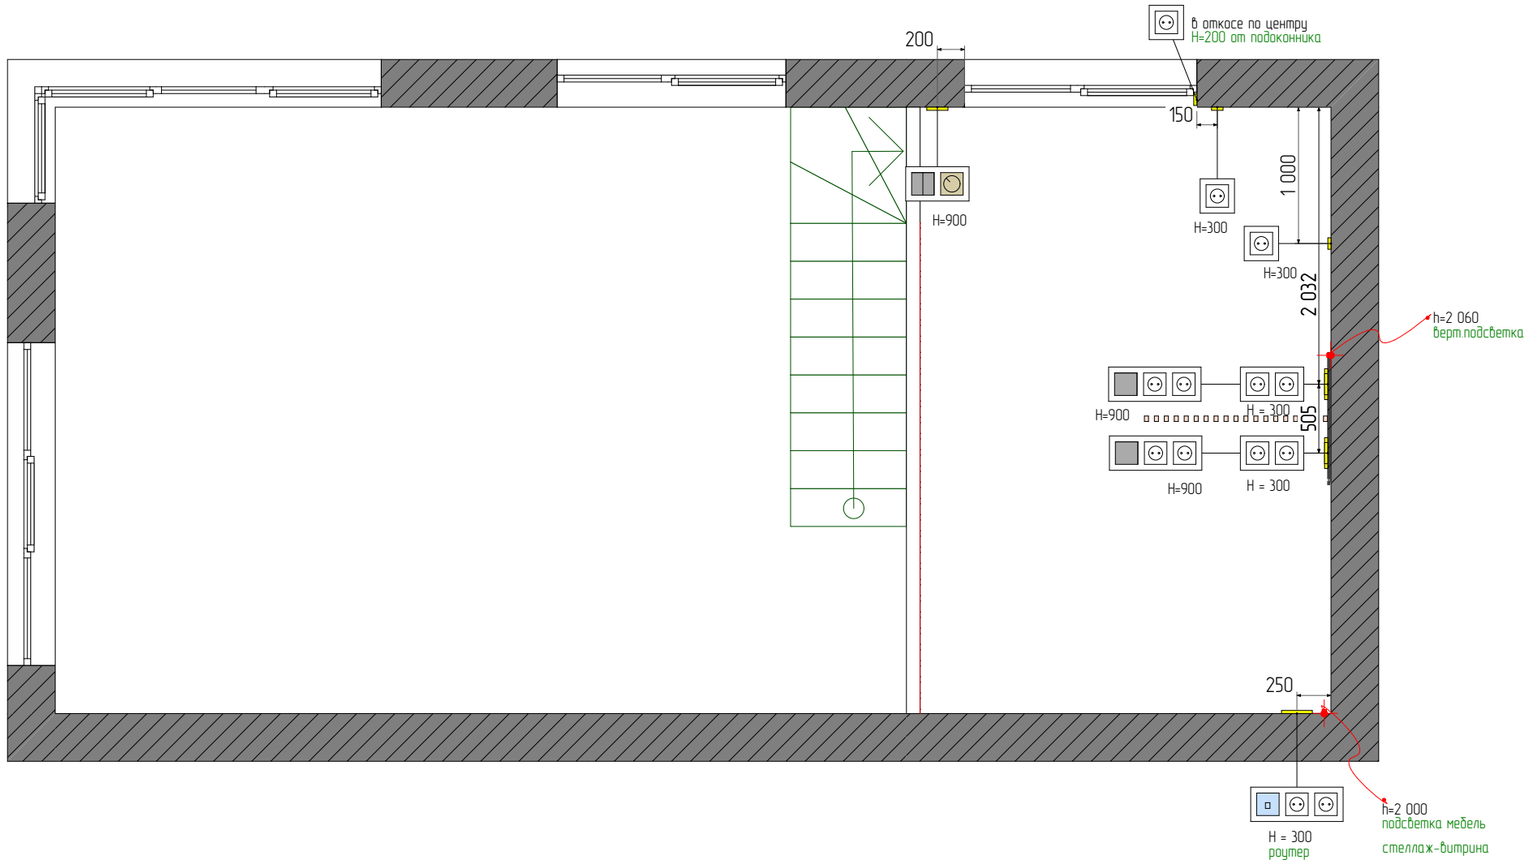

Условное обозначение	Наименование	Кол-во, шт
	Вывод для домофона	1
	Интернет-розетка RJ45	1
	Розетка 220V + USB	3
	Розетка бытовая 220 V	46
	Силовой кабель	1
	Эл.щит/слаботочный щит	1
	Электровывод	15

Выключатели 1 этаж+ антресоль		
Условное обозначение	Наименование	Кол-во, шт
	Выключатель двухклавишный	1
	Выключатель двухклавишный проходной	2
	Выключатель одноклавишный	5
	Выключатель одноклавишный проходной	3
	Мастер-выключатель	1
	Самовозвратный выключатель	9

Рамки (общее количество)		
Тип рамки (блока)	Рамка ориентация	Кол-во
Рамка х1	Горизонтальная	15
Рамка х2	Горизонтальная	11
Рамка х3	Горизонтальная	7
Рамка х4	Горизонтальная	2
Рамка х5	Горизонтальная	1
		36

Примечание:

1. Все размеры указаны в миллиметрах, по осям и в чистом виде.
2. Высотные отметки указаны от уровня чистового пола до центра группы розеток, если на плане не указано иное.
3. Перед началом работ все разметки и отметки проверить по месту.
4. Розетки и выключатели устанавливать блоками.
5. В санузле использовать влагозащищенные розетки.
6. Все рамки читать слева-направо, сверять расположение по разверткам.
7. Демонтировать существующие розетки и выключатели.
8. Размещение электровыводов вентиляции согласовать с соответствующими специалистами.
9. Размещение электровыводов для электрокарнизов согласовать с соответствующими специалистами после выбора конкретной модели карнизов. Предпочтительное размещение - в нише потолка со стороны размещения моторов.
10. Расположение розеток в кухне согласовать с производителем кухни.
11. Точное расположение бризеров и выводов для него согласовать со специалистом и Заказчиком.
12. Расположение роутера согласовать со специалистом и Заказчиком.
13. Для подключения электрической варочной панели и духового шкафа предусмотреть силовой кабель и развести на отдельные автоматы в электрощите.
14. Точное расположение и размеры электрощита подбирает электромонтажник, исходя из количества размещаемых автоматов.
15. В откосах окон использовать БЕЛЫЕ розетки.
16. Размещение накладной розетки за ТВ-тумбой определить на месте после установки тумбы.
17. В спецификациях указано общее количество выключателей/розеток/рамок для 1 этажа и антресоли.

Проект	гп Новоселье, Бульвар Белых ночей, д.3, кв.319	План размещения электрических розеток и выключателей антресоль	Масштаб	Лист	Листов
Дизайнер	Ирина Лобанова		1:45	20	63
телефон	+7-953-902-05-38		Дата	16.03.2026	

План потолков с указанием типа используемых материалов 1 этаж

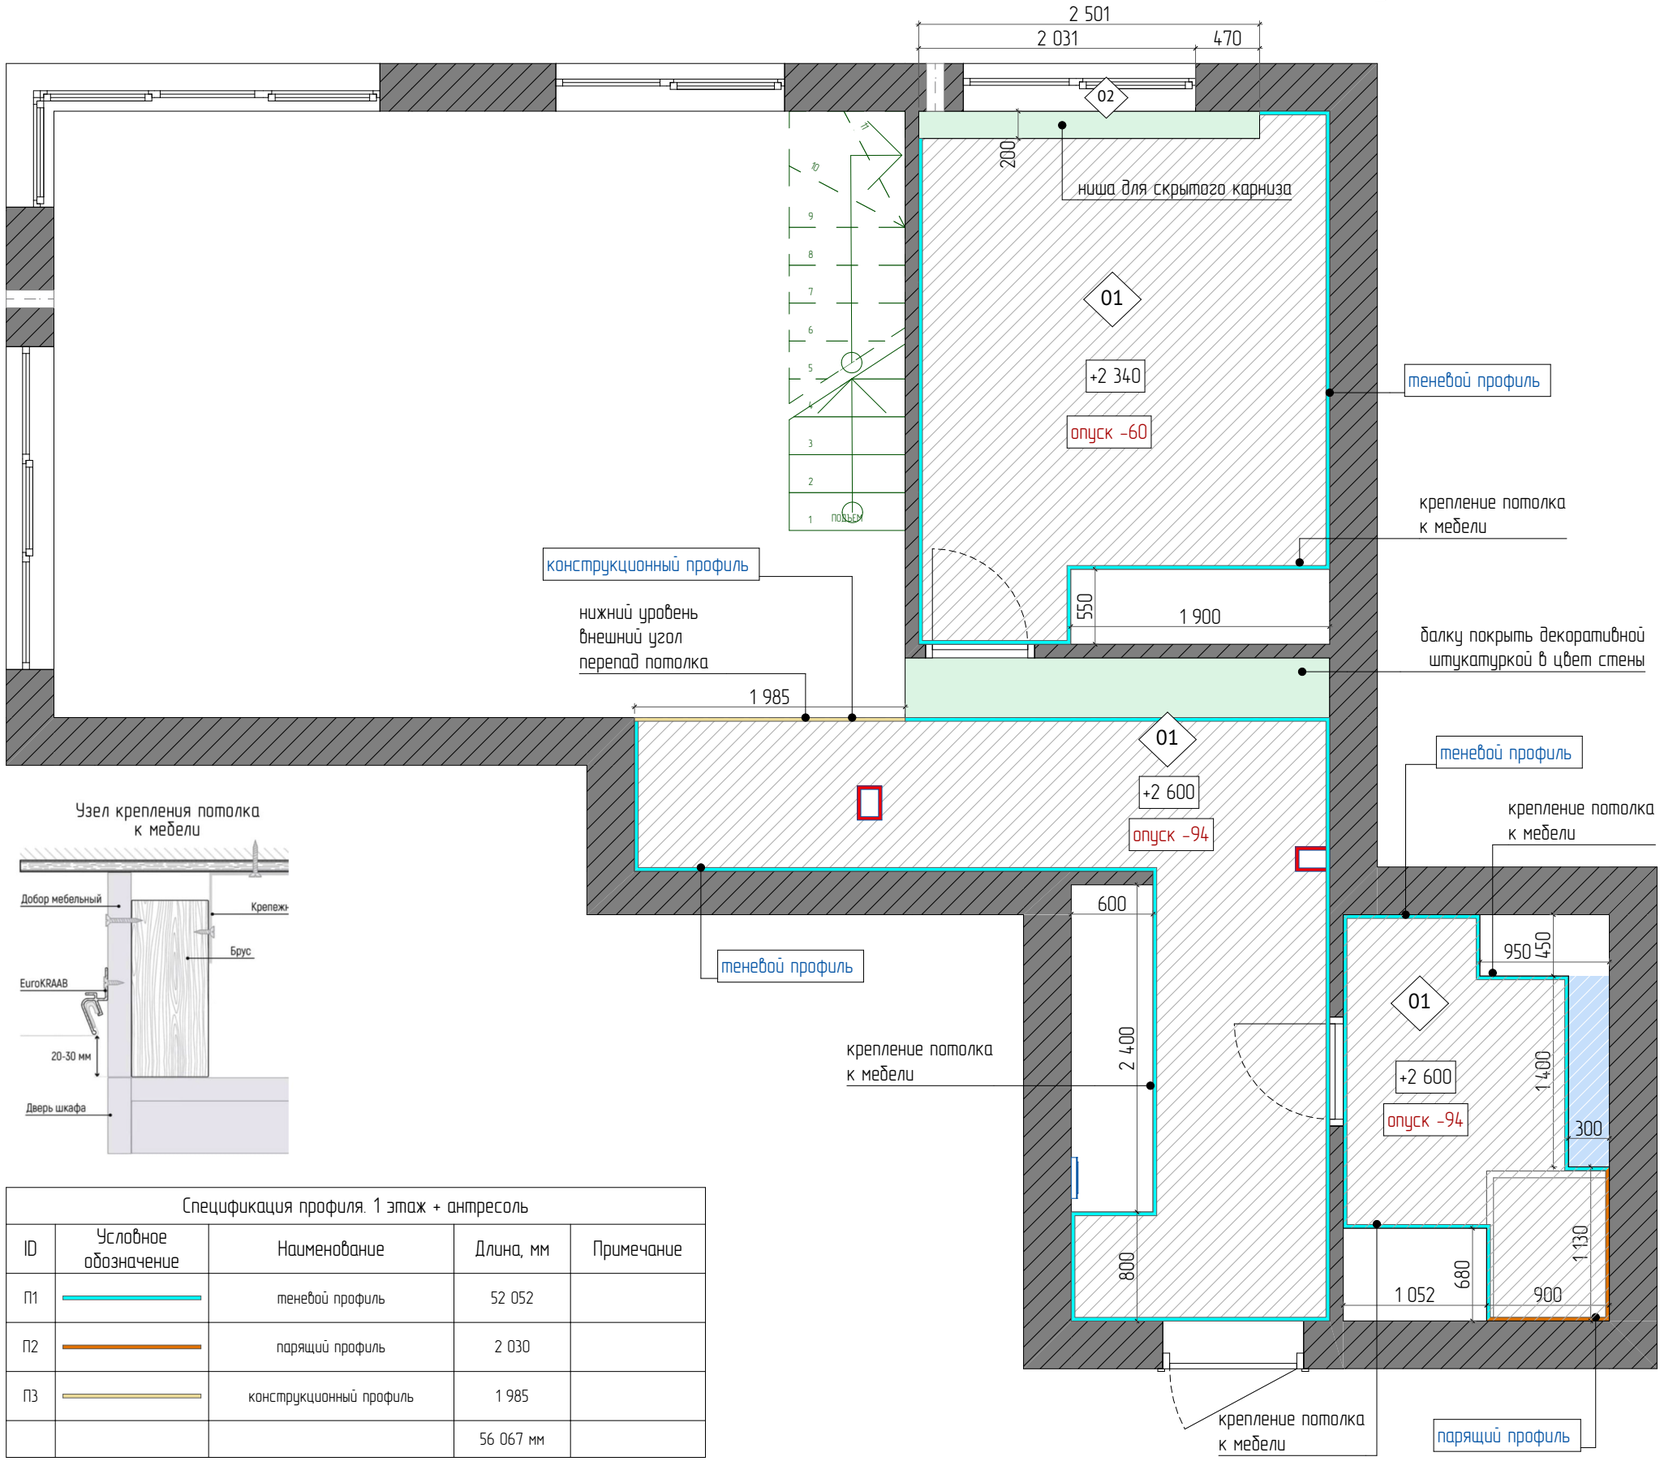

Узел крепления потолка
к мебели

Ведомость потолков. 1 этаж + антресоль			
ID	Условное обозначение	Наименование	S нетто, кв.м (без запаса)
01		Потолок натяжной ПВХ	62,77
02		Оштукатуренный и окрашенный потолок	4,46
03		Закладная под рейки и светильники	0,14

Условные обозначения:

02 – обозначение типа потолка

+2 900 – отметка высоты относительно чистового пола

Примечание:

1. Все размеры указаны в миллиметрах, по осям и в чистом виде.
2. Высотные отметки указаны от уровня чистового пола.
3. Перед началом работ все разметки и отметки проверить по месту.
4. Несоответствие размеров и отметок согласовать с дизайнером.
5. Чертеж читать вместе с планом размещения осветительных приборов.
6. Вентиляционные решетки в потолке расположить с учетом расположения световых линий на плане освещения и согласовать с Заказчиком.
7. Точное количество и тип потолочных профилей согласовать со специалистом по потолкам и Заказчиком.
8. Точную величину опуска потолка определяет специалист по потолкам на месте. Рекомендовано закладывать минимально возможный опуск.
9. Закладную для реечной перегородки сделать из ровного, сухого, строганного деревянного бруса. Металлическую не использовать. Закрепить жестко, на металлических уголках, мягкие подвесы не использовать. При физическом воздействии на закладную (надавливании рукой), она не должна менять своего начального положения.
10. Установку конструкционного профиля в месте перепада потолка осуществить на стадии черновых работ после штукатурки. ПРОКОНСУЛЬТИРОВАТЬСЯ СО СПЕЦИАЛИСТОМ ПО ПОТОЛКАМ ЗАРАНЕЕ!

Спецификация профиля. 1 этаж + антресоль				
ID	Условное обозначение	Наименование	Длина, мм	Примечание
П1		теневой профиль	52 052	
П2		парящий профиль	2 030	
П3		конструкционный профиль	1 985	
			56 067 мм	

Проект	гп Новоселье, Бульвар Белых ночей, д.3, кв.319	План потолков с указанием типа используемых материалов 1 этаж	Масштаб	Лист	Листов
Дизайнер	Ирина Лобанова		1:45	21	63
телефон	+7-953-902-05-38		Дата	16.03.2026	

План потолков с указанием типа используемых материалов антресоль

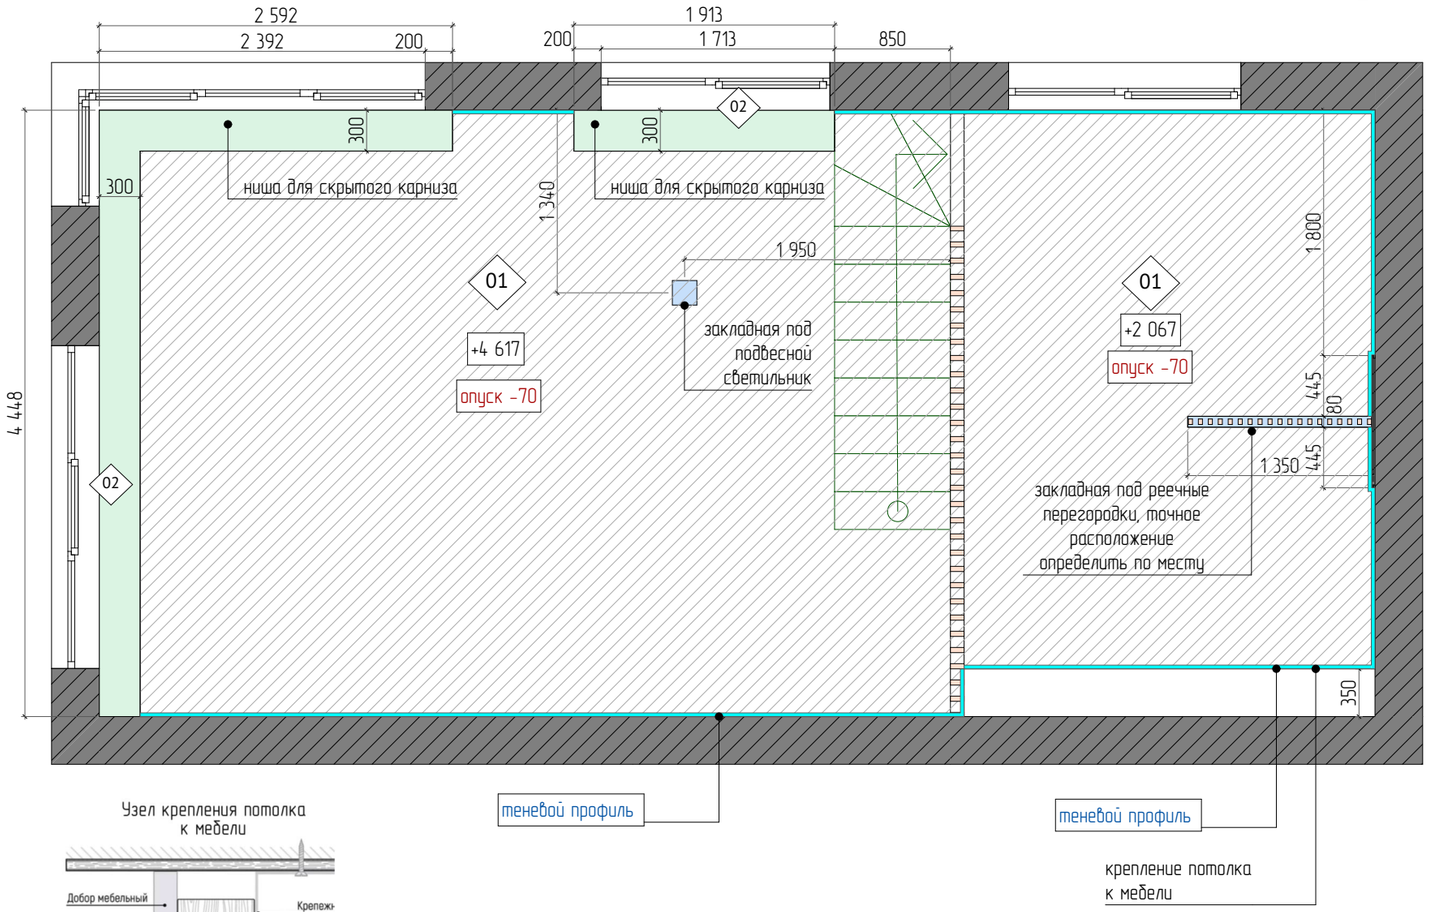

Узел крепления потолка к мебели

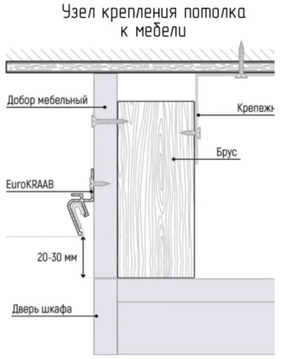

Ведомость потолков. 1 этаж + антресоль			
ID	Условное обозначение	Наименование	S нетто, кв.м (без запаса)
01		Потолок натяжной ПВХ	62,77
02		Оштукатуренный и окрашенный потолок	4,46
03		Закладная под рейки и светильники	0,14

Условные обозначения:

02 - обозначение типа потолка

+2 900 - отметка высоты относительно чистового пола

Спецификация профиля. 1 этаж + антресоль				
ID	Условное обозначение	Наименование	Длина, мм	Примечание
П1		теневой профиль	52 052	
П2		парящий профиль	2 030	
П3		конструкционный профиль	1 985	
			56 067 мм	

Примечание:

1. Все размеры указаны в миллиметрах, по осям и в чистом виде.
2. Высотные отметки указаны от уровня чистового пола.
3. Перед началом работ все разметки и отметки проверить по месту.
4. Несоответствие размеров и отметок согласовать с дизайнером.
5. Чертеж читать вместе с планом размещения осветительных приборов.
6. Вентиляционные решетки в потолке расположить с учетом расположения световых линий на плане освещения и согласовать с Заказчиком.
7. Точное количество и тип потолочных профилей согласовать со специалистом по потолкам и Заказчиком.
8. Точную величину опуска потолка определяет специалист по потолкам на месте. Рекомендовано закладывать минимально возможный опуск.
9. Закладную для реечной перегородки сделать из ровного, сухого, строганного деревянного бруса. Металлическую не использовать. Закрепить жестко, на металлических уголках, мягкие подвесы не использовать. При физическом воздействии на закладную (надавливании рукой), она не должна менять своего начального положения.
10. Установку конструкционного профиля в месте перепада потолка осуществить на стадии черновых работ после штукатурки. ПРОКОНСУЛЬТИРОВАТЬСЯ СО СПЕЦИАЛИСТОМ ПО ПОТОЛКАМ ЗАРАНЕЕ!

Проект	гп Новоселье, Бульвар Белых ночей, д.3, кв.319	План потолков с указанием типа используемых материалов антресоль	Масштаб	Лист	Листов
Дизайнер	Ирина Лобанова		1:45	22	63
телефон	+7-953-902-05-38		Дата	16.03.2026	