План расположения систем отопления и вентиляции

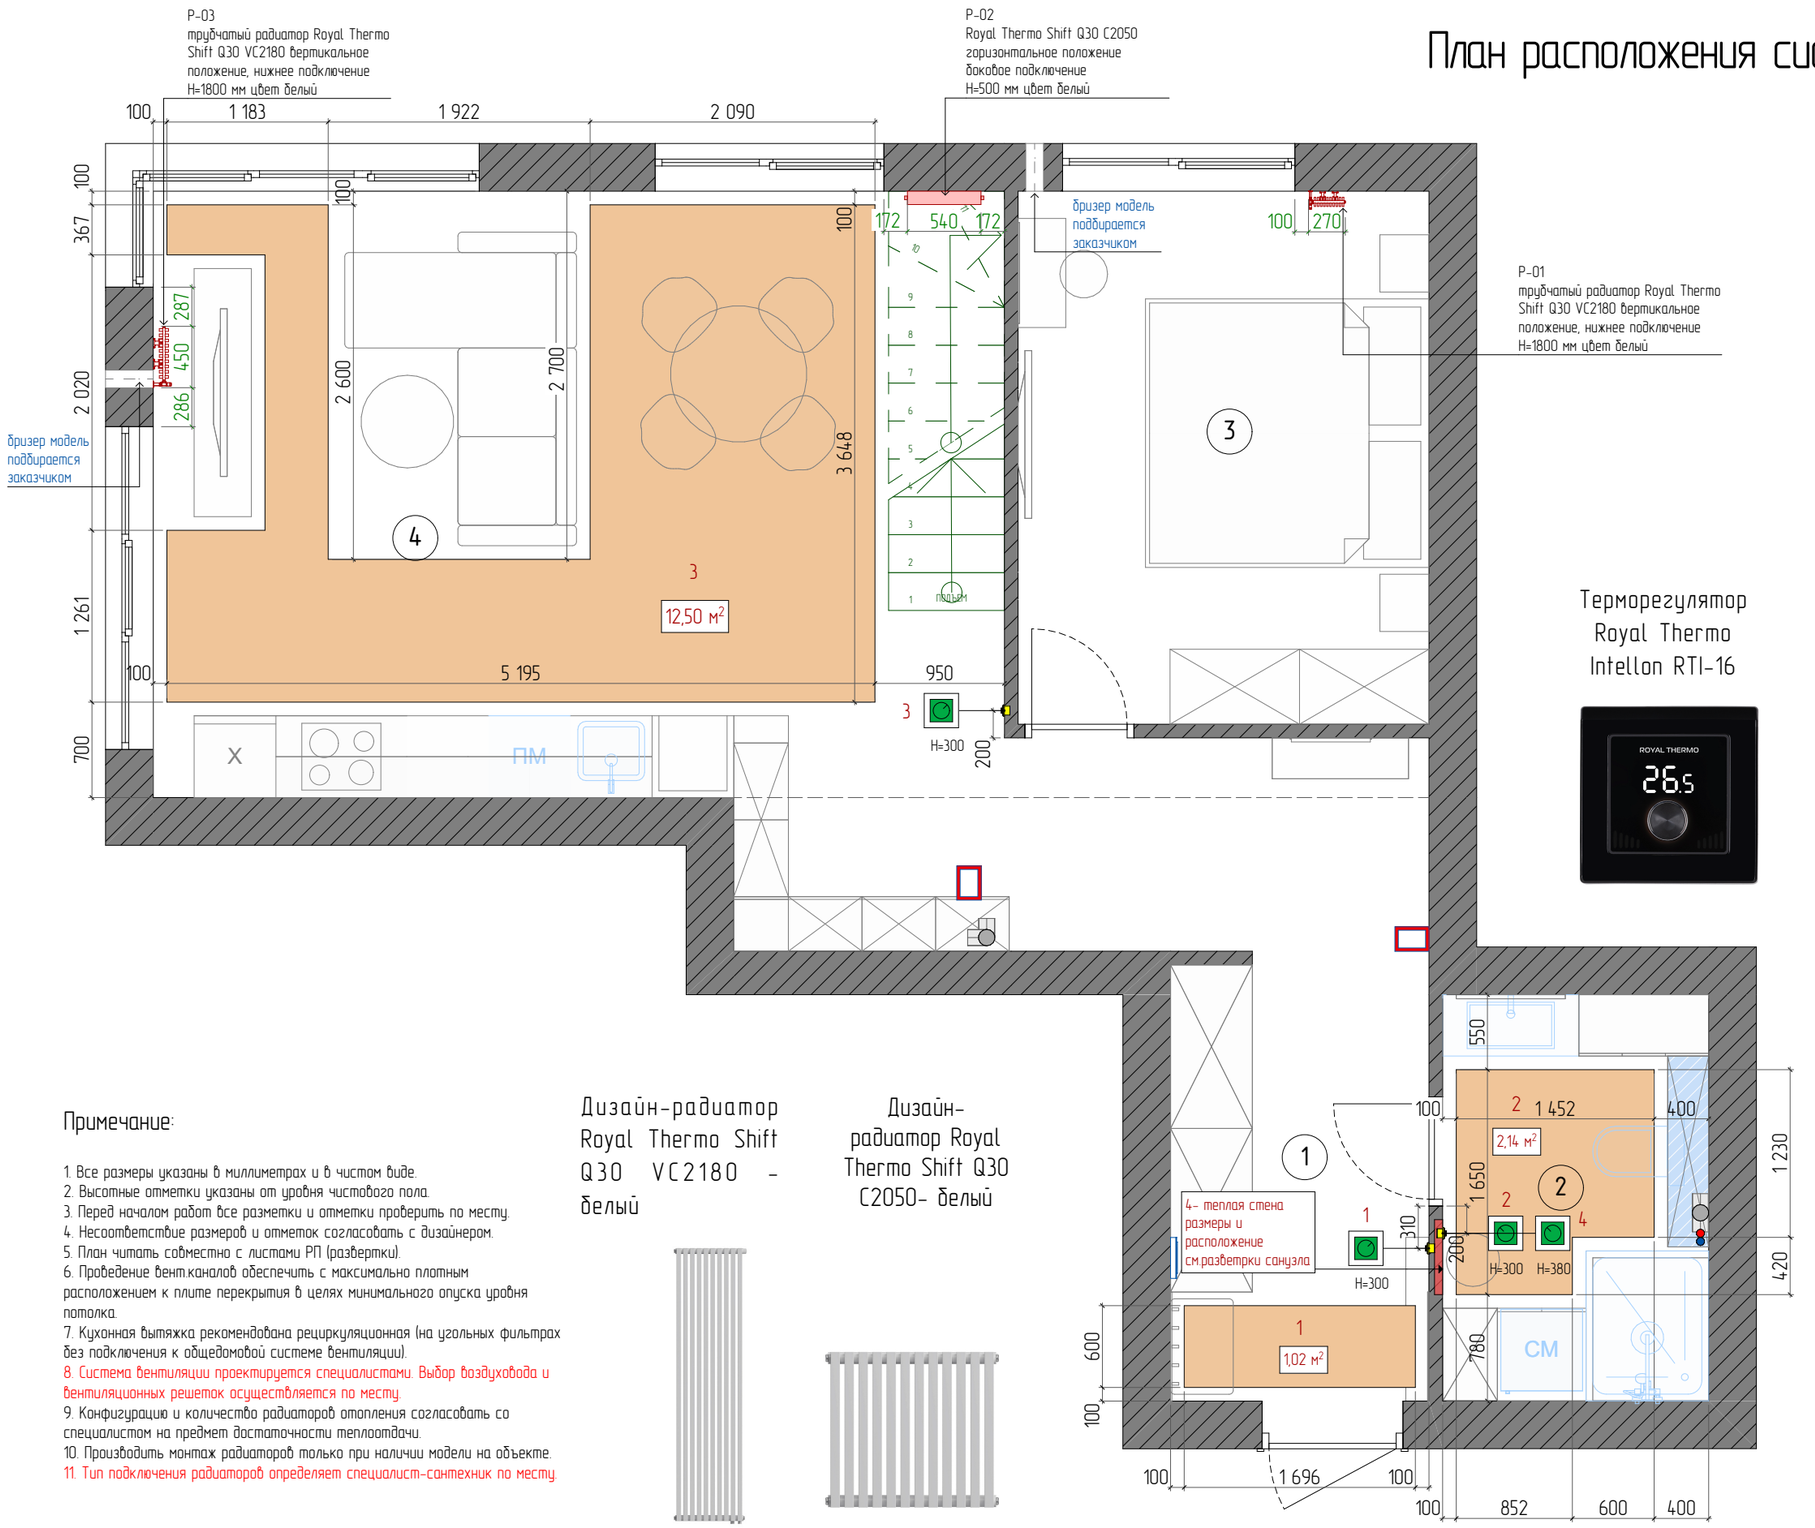

Экспликация помещений 1 этаж		
№	Название помещения	S, кв.м
1	Прихожая	6,20
2	Санузел	5,40
3	Спальня	11,79
4	Кухня-гостиная	34,89
		58,28 м²

Терморегулятор Royal Thermo Intellon RTI-16

Теплый пол. 1 этаж		
Условное обозначение	Наименование	S, кв.м/ кол-во, шт
	Электрический тёплый пол	15,66
	Электрическая теплая стена	0,55
		16,21 м²

Регулятор тёплого пола/стены. 1 этаж		
Условное обозначение	Наименование	Кол-во, шт
	Регулятор теплого пола/стены	4

Дизайн-радиатор Royal Thermo Shift Q30 VC2180 - белый

Дизайн-радиатор Royal Thermo Shift Q30 C2050- белый

Примечание:

1. Все размеры указаны в миллиметрах и в чистом виде.
2. Высотные отметки указаны от уровня чистового пола.
3. Перед началом работ все разметки и отметки проверить по месту.
4. Несоответствие размеров и отметок согласовать с дизайнером.
5. План читать совместно с листами РП (развертки).
6. Проведение вент.каналов обеспечить с максимально плотным расположением к плите перекрытия в целях минимального опуска уровня потолка.
7. Кухонная вытяжка рекомендована рециркуляционная (на угольных фильтрах без подключения к общедомовой системе вентиляции).
8. Система вентиляции проектируется специалистами. Выбор воздуховода и вентиляционных решеток осуществляется по месту.
9. Конфигурацию и количество радиаторов отопления согласовать со специалистом на предмет достаточности теплоотдачи.
10. Производить монтаж радиаторов только при наличии модели на объекте.
11. Тип подключения радиаторов определяет специалист-сантехник по месту.

Условные обозначения:

- радиатор отопления вертикальный
- радиатор отопления горизонтальный

Проект	гп Новоселье, Бульвар Белых ночей, д.3, кв.319	План расположения систем отопления и вентиляции	Масштаб	Лист	Листов
Дизайнер	Ирина Лобанова		1:45	25	60
телефон	+7-953-902-05-38		Дата	16.03.2026	